


CIRCUITO GENERAL

Esquema de conexión de todos los componentes del sistema

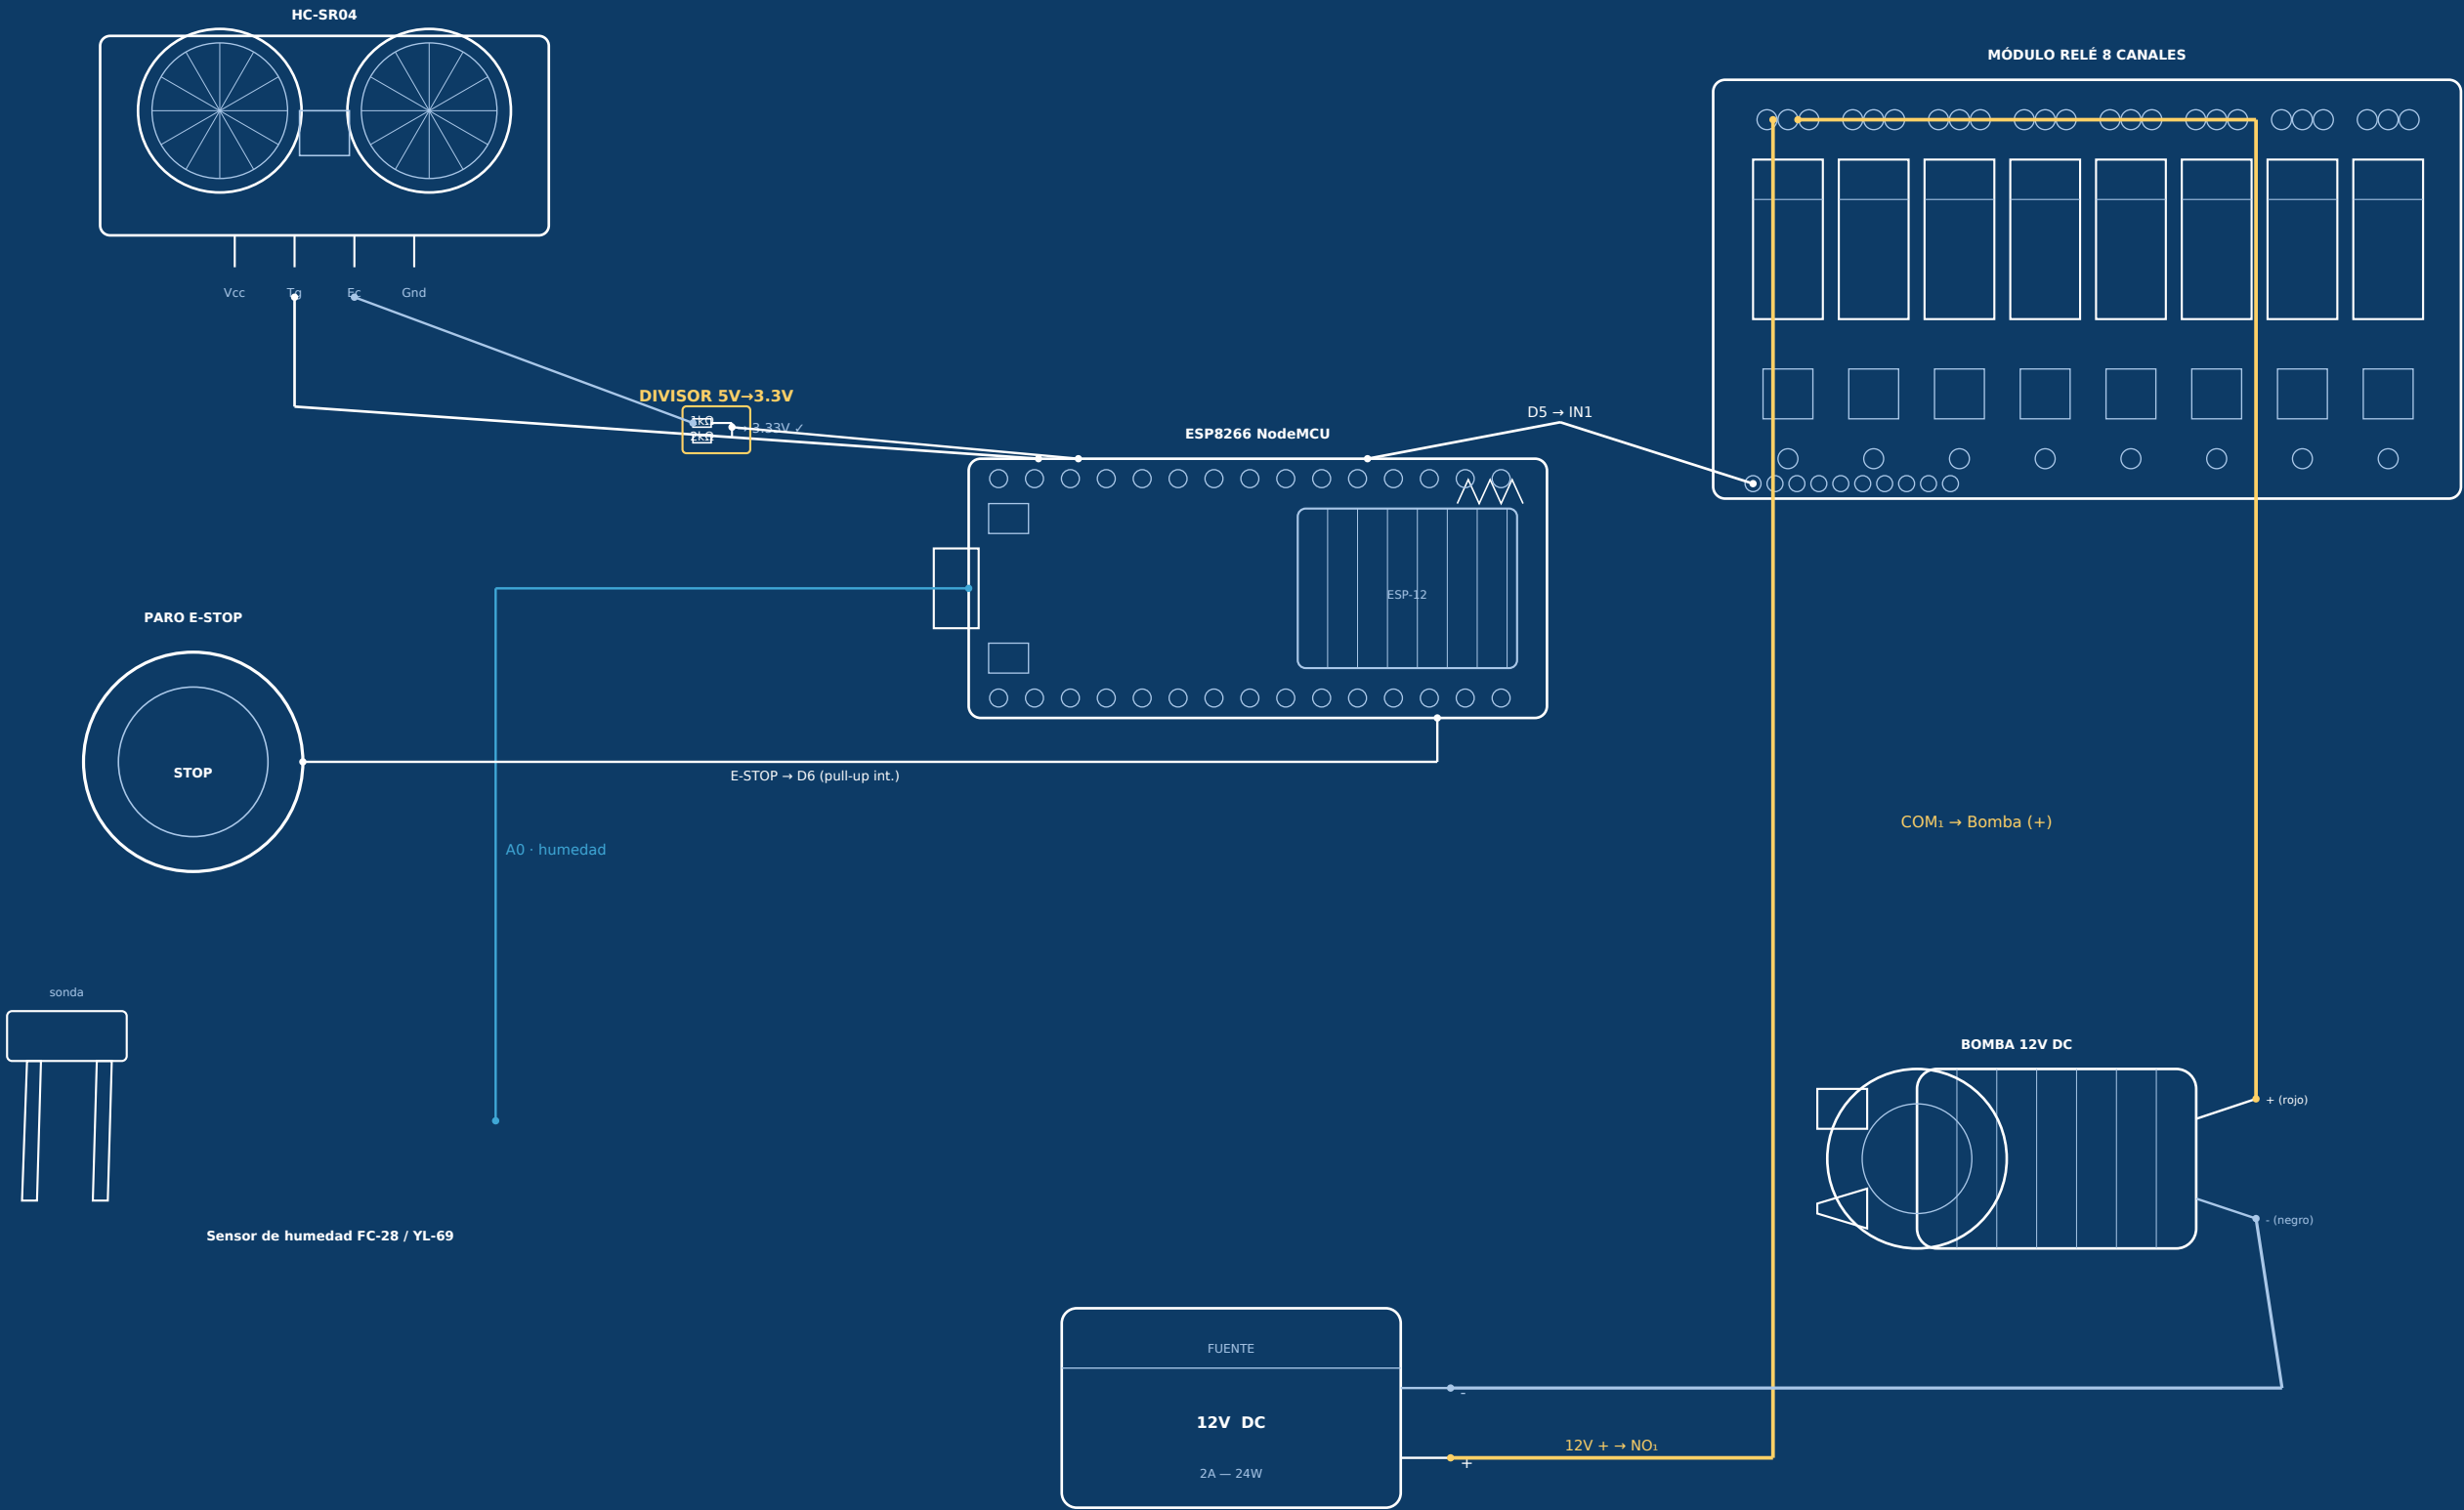

LEYENDA

- Señal digital / control (3.3-5V)
- Señal analógica (A0 humedad)
- Potencia 12V DC (bomba)
- Retorno común / GND

AquaGuard

Automatización de llenado de tanques

CONEXIONADO GENERAL

PLANO 01/04

ESC: S/E
COTAS EN mm

16/06/2026
Proyecto Universidad

A3